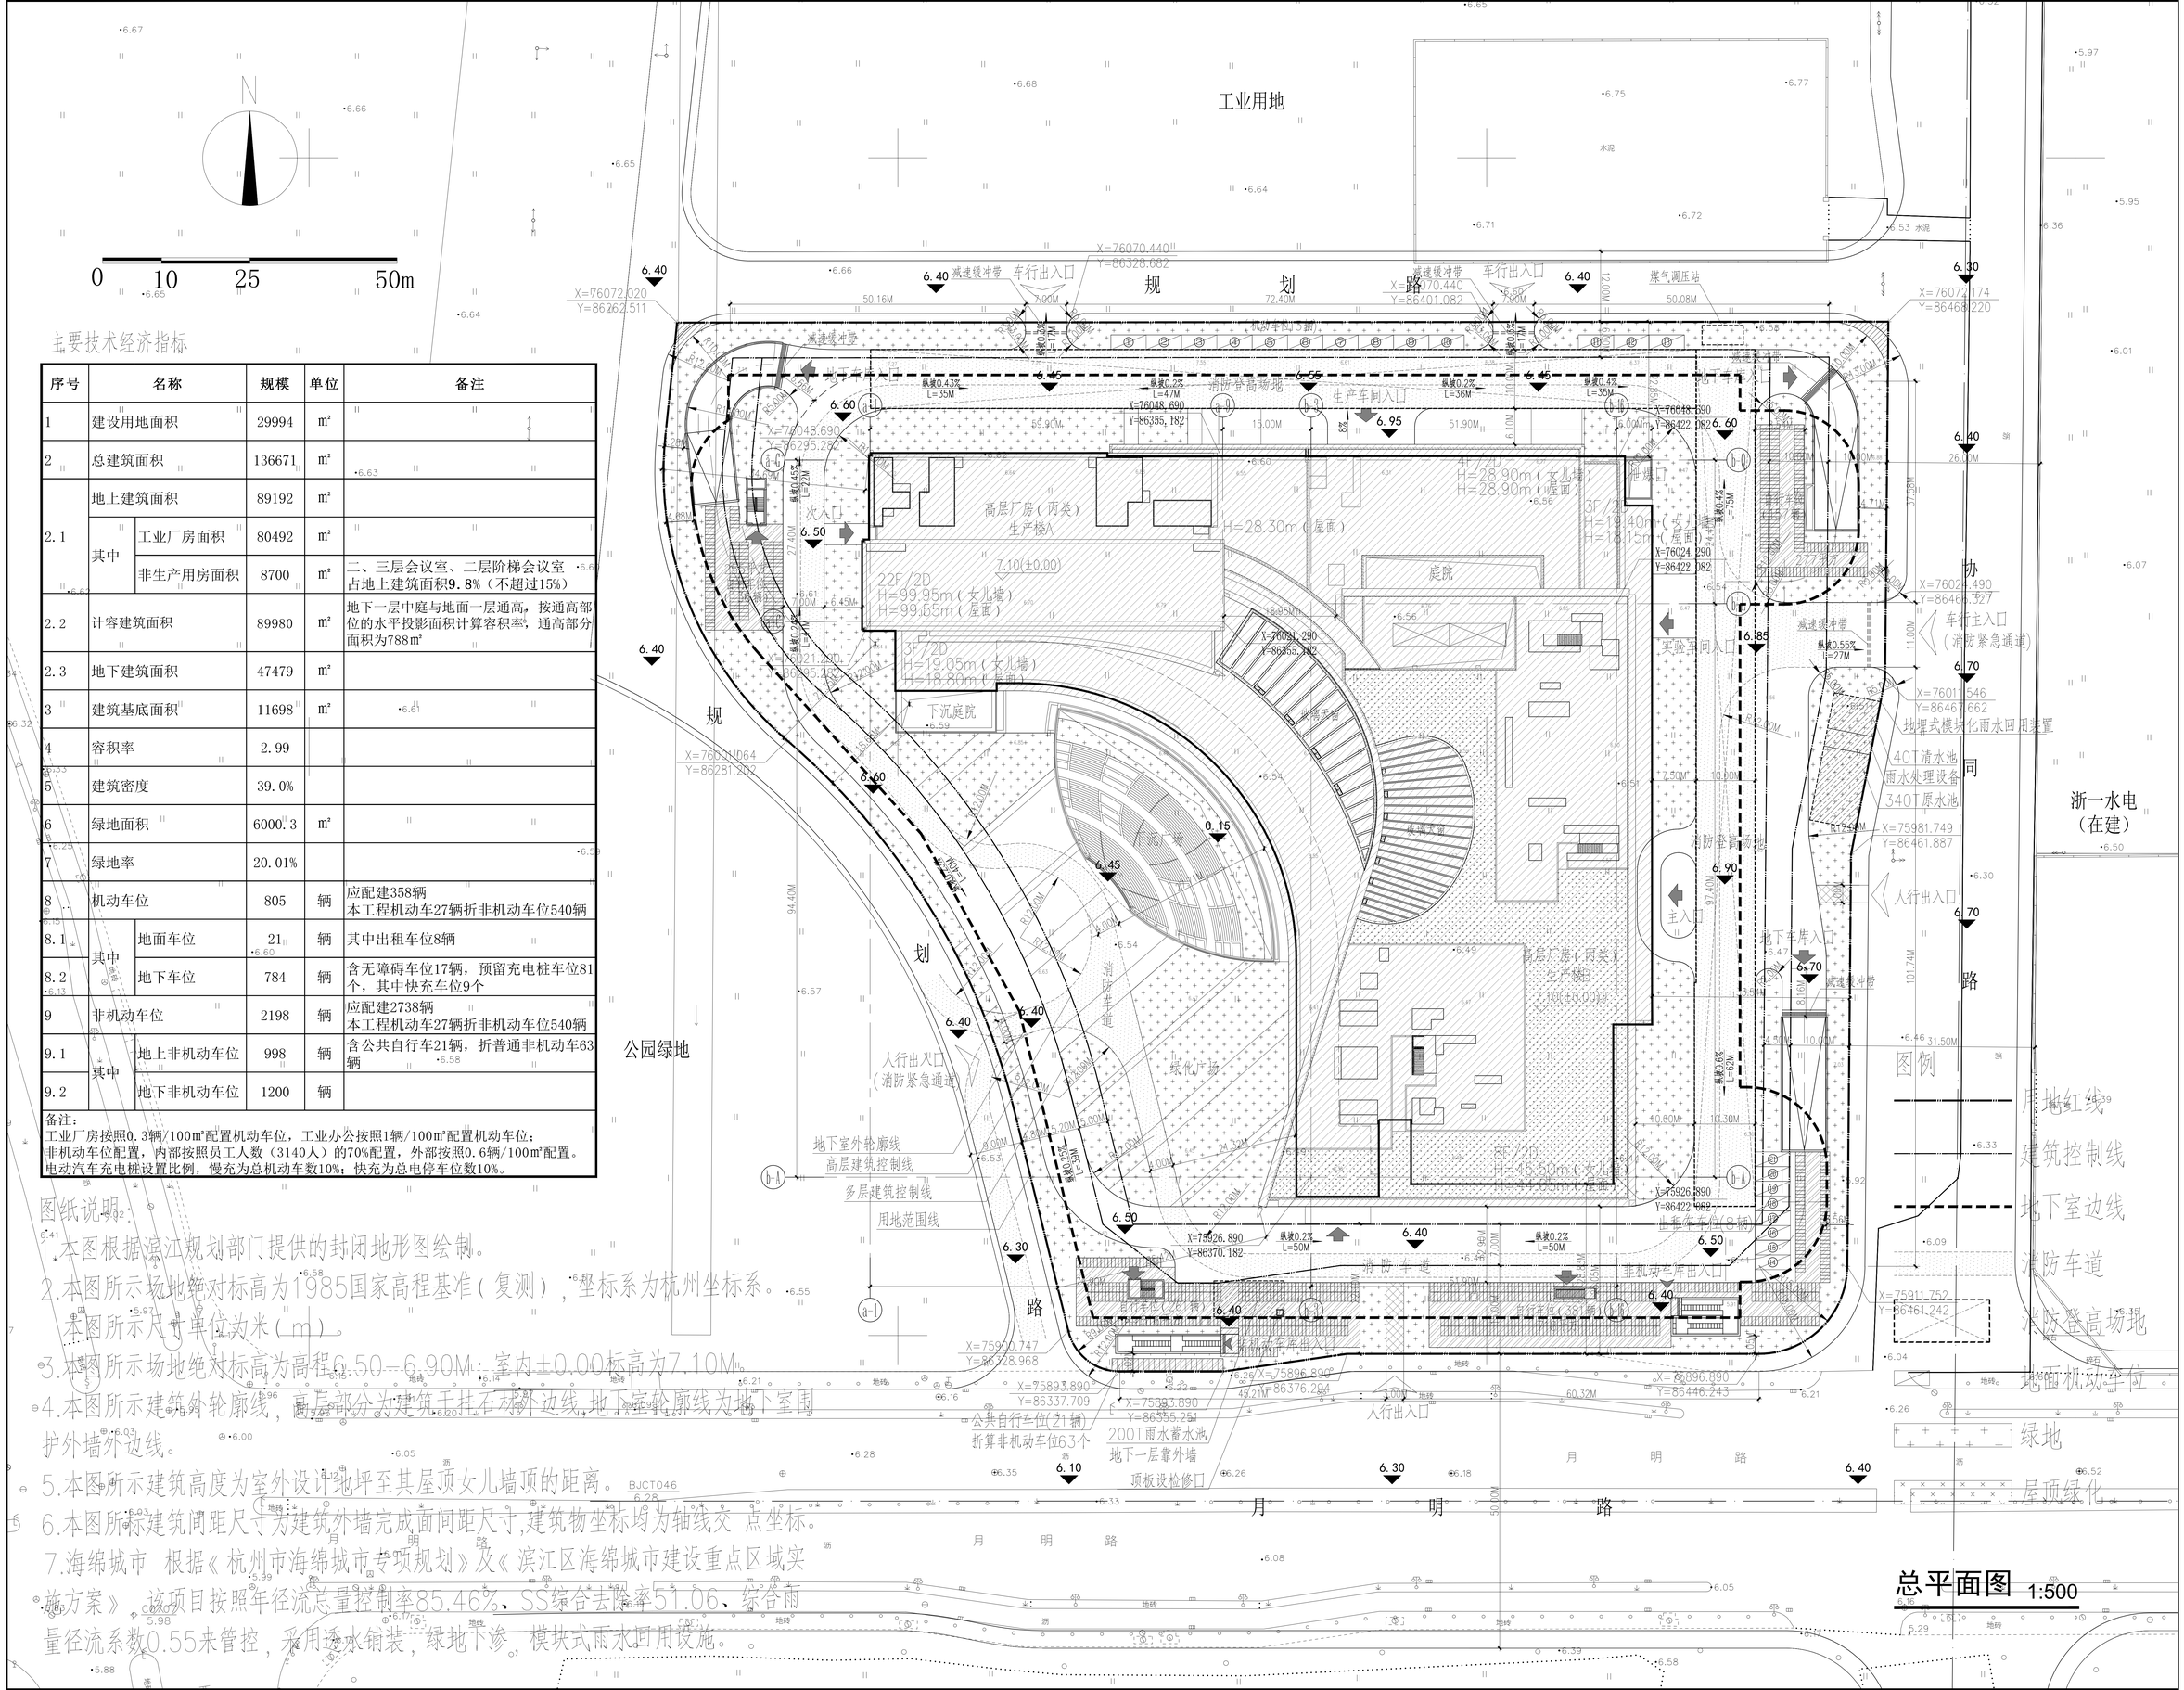


主要技术经济指标

序号	名称		规模	单位	备注
1	建设用地面积		29994	㎡	
2	总建筑面积		136671	㎡	
2.1	地上建筑面积		89192	㎡	
	其中	工业厂房面积	80492	㎡	
		非生产用房面积	8700	㎡	二、三层会议室、二层阶梯会议室占地上建筑面积9.8%（不超过15%）
2.2	计容建筑面积		89980	㎡	地下一层中庭与地面一层通高，按通高部位的水平投影面积计算容积率，通高部分面积为788㎡
2.3	地下建筑面积		47479	㎡	
3	建筑基底面积		11698	㎡	
4	容积率		2.99		
5	建筑密度		39.0%		
6	绿地面积		6000.3	㎡	
7	绿地率		20.01%		
8	机动车位		805	辆	应配建358辆 本工程机动车27辆折非机动车位540辆
8.1	其中	地面车位	21	辆	其中出租车位8辆
8.2		地下车位	784	辆	含无障碍车位17辆，预留充电桩车位81个，其中快充车位9个
9	非机动车位		2198	辆	应配建2738辆 本工程机动车27辆折非机动车位540辆
9.1	其中	地上非机动车位	998	辆	含公共自行车21辆，折普通非机动车63辆
9.2		地下非机动车位	1200	辆	

备注：
工业厂房按照0.3辆/100㎡配置机动车位，工业办公按照1辆/100㎡配置机动车位；
非机动车位配置，内部按照员工人数（3140人）的70%配置，外部按照0.6辆/100㎡配置。
电动汽车充电桩设置比例，慢充为总机动车数10%；快充为总电停车位数10%。

图纸说明：

1.本图根据滨江规划部门提供的封闭地形图绘制。

2.本图所示场地绝对标高为1985国家高程基准（复测），坐标系为杭州坐标系。本图所示尺寸单位为米（m）。

3.本图所示场地绝对标高为高程6.50—6.90M；室内±0.00标高为7.10M。

4.本图所示建筑外轮廓线，高层部分为建筑干挂石材外边线，地下室轮廓线为地下室围护外墙外边线。

5.本图所示建筑高度为室外设计地坪至其屋顶女儿墙顶的距离。

6.本图所标建筑间距尺寸为建筑外墙完成面间距尺寸，建筑物坐标均为轴线交点坐标。

7.海绵城市 根据《杭州市海绵城市专项规划》及《滨江区海绵城市建设重点区域实施方案》，该项目按照年径流总量控制率85.46%、SS综合去除率51.06、综合雨量径流系数0.55来管控，采用透水铺装，绿地下沉，模块式雨水回用设施。

总平面图 1:500